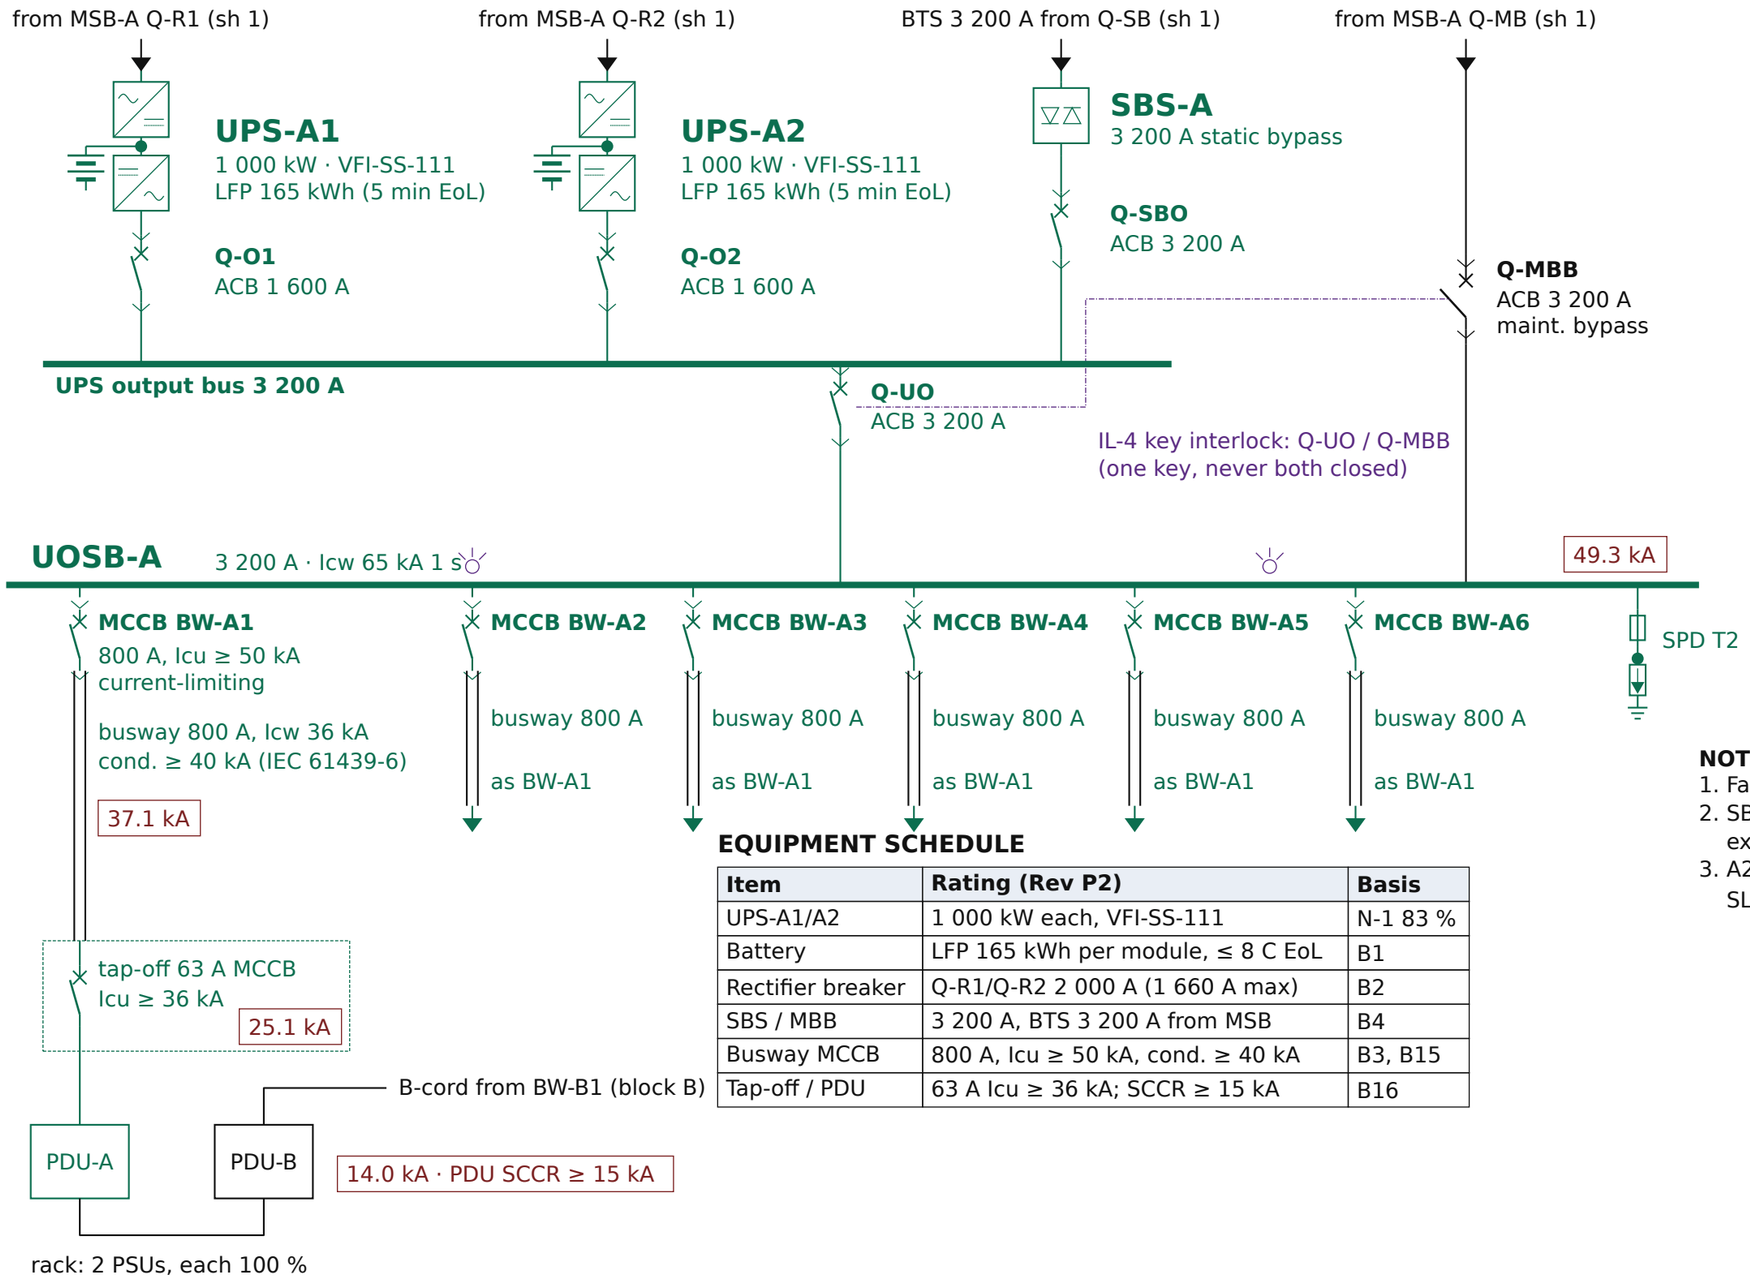

EQUIPMENT SCHEDULE

Item	Rating (Rev P2)	Basis
UPS-A1/A2	1 000 kW each, VFI-SS-111	N-1 83 %
Battery	LFP 165 kWh per module, ≤ 8 C EoL	B1
Rectifier breaker	Q-R1/Q-R2 2 000 A (1 660 A max)	B2
SBS / MBB	3 200 A, BTS 3 200 A from MSB	B4
Busway MCCB	800 A, Icu ≥ 50 kA, cond. ≥ 40 kA	B3, B15
Tap-off / PDU	63 A Icu ≥ 36 kA; SCCR ≥ 15 kA	B16

NOTES

1. Fault levels in boxes: I″k per CALC-003.
2. SBS is centralised per block; MBB is external wrap-around (IL-4).
3. A2…A6 identical to BW-A1; pairing per SLD-002 sh 2.

P2	2026-10-25	CALC-002/3/4 ratings, IEC symbols, ≥2.5 mm text
P1	2026-10-24	First concept issue

Nordic Hyperscale DC Campus (fictional) · 30 MW IT · SE3

Portfolio D. Wu · public standards and [ASSUMED] data only

Power block A — sheet 2

UPS-A1/A2, SBS, MBB, UOSB-A, busway to rack (typical)

CONCEPT · NOT FOR CONSTRUCTION · scale NTS · A3

Drawing no.	Sheet	Rev
DWU-DC-E-SLD-003	**2 / 2**	**P2**