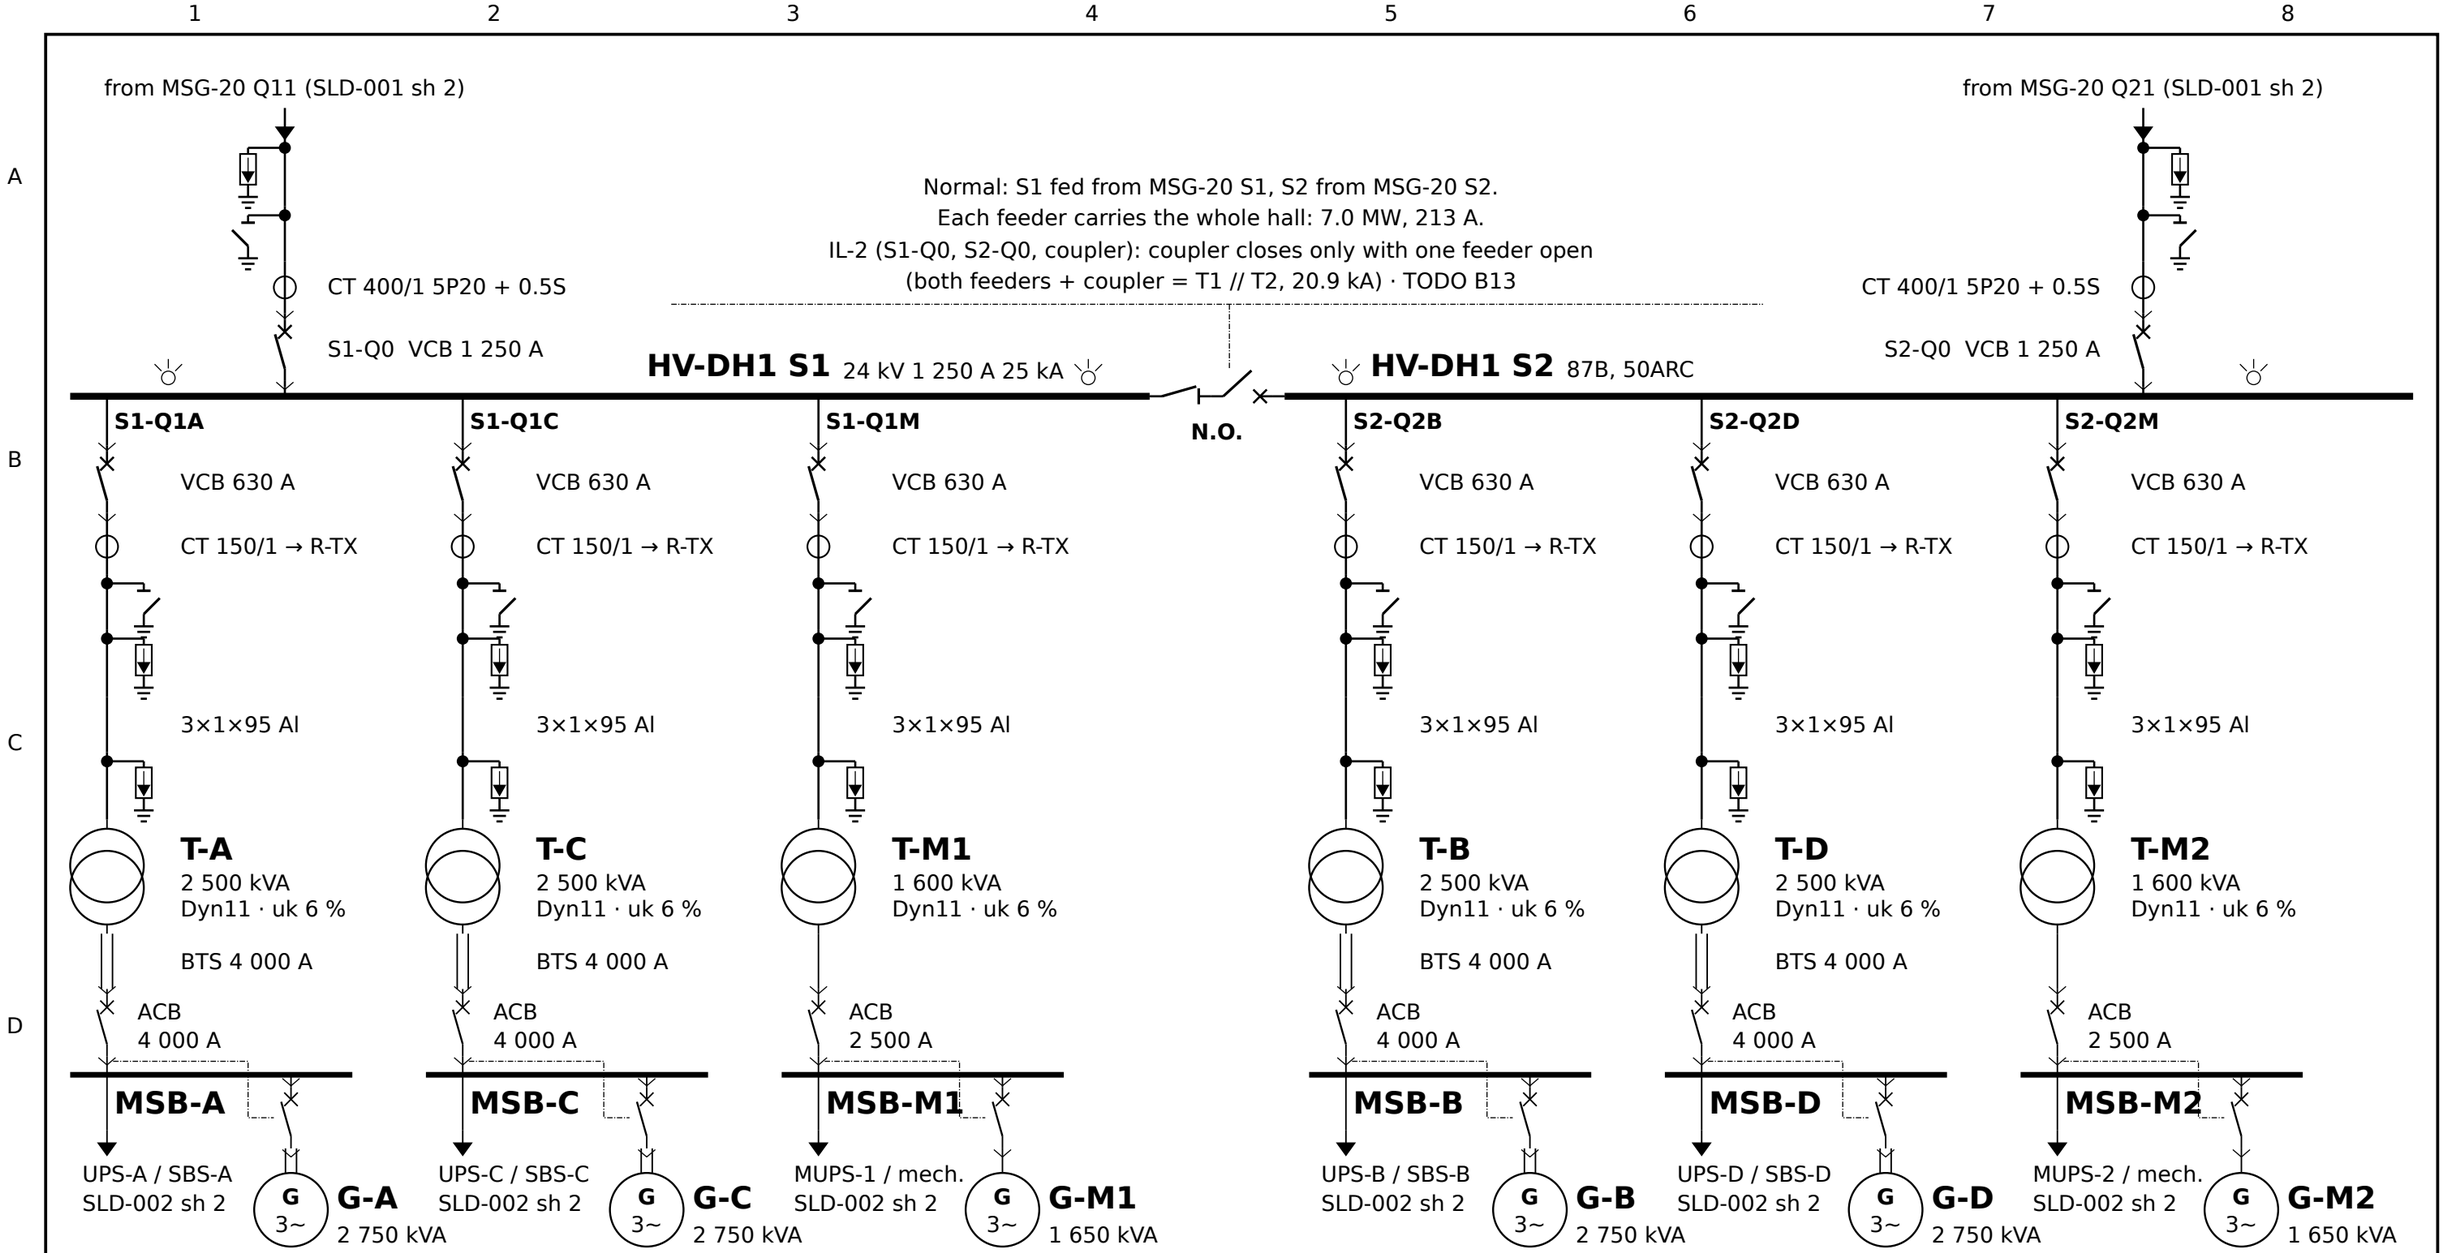

ATS (dash-dot): transformer ACB / genset ACB, open transition only (TODO B14). Gensets via BTS 4 000 A (B5).

Item	Rating (Rev P2)	Check (CALC-002/3)
T-A…T-D	2 500 kVA 20/0.42 kV Dyn11, uk 6 %, Pk 19 kW	N-1 82 %
G-A…G-D	2 750 kVA / 2 200 kWe DCC, Isc ≥ 300 % 2 s	N-1 88 %
MSB-A…D	4 000 A, Icw 65 kA 1 s, Ipk 143 kA	52.3 kA
UPS-A…D	2 × 1 000 kW, 2 × 165 kWh LFP	N-1 83 %
UOSB-A…D	3 200 A, 65 kA 1 s	49.3 kA
T-M1/M2	1 600 kVA kept (1 250 kVA would be 83 %)	65 %
G-M / MUPS	1 650 kVA; mech. UPS 2 × 250 kW	step ≤ 33 %

P2	2026-10-25	CALC-002/3/4 ratings, IEC symbols, ≥2.5 mm text
P1	2026-10-24	First concept issue

Nordic Hyperscale DC Campus (fictional) · 30 MW IT · SE3
Portfolio D. Wu · public standards and [ASSUMED] data only

Data hall DH-1 — sheet 1
HV-DH1, IT power blocks A–D (4N/3), mechanical 2N
CONCEPT · NOT FOR CONSTRUCTION · scale NTS · A3

Drawing no.	Sheet	Rev
DWU-DC-E-SLD-002	**1 / 2**	**P2**